



SITE PLAN

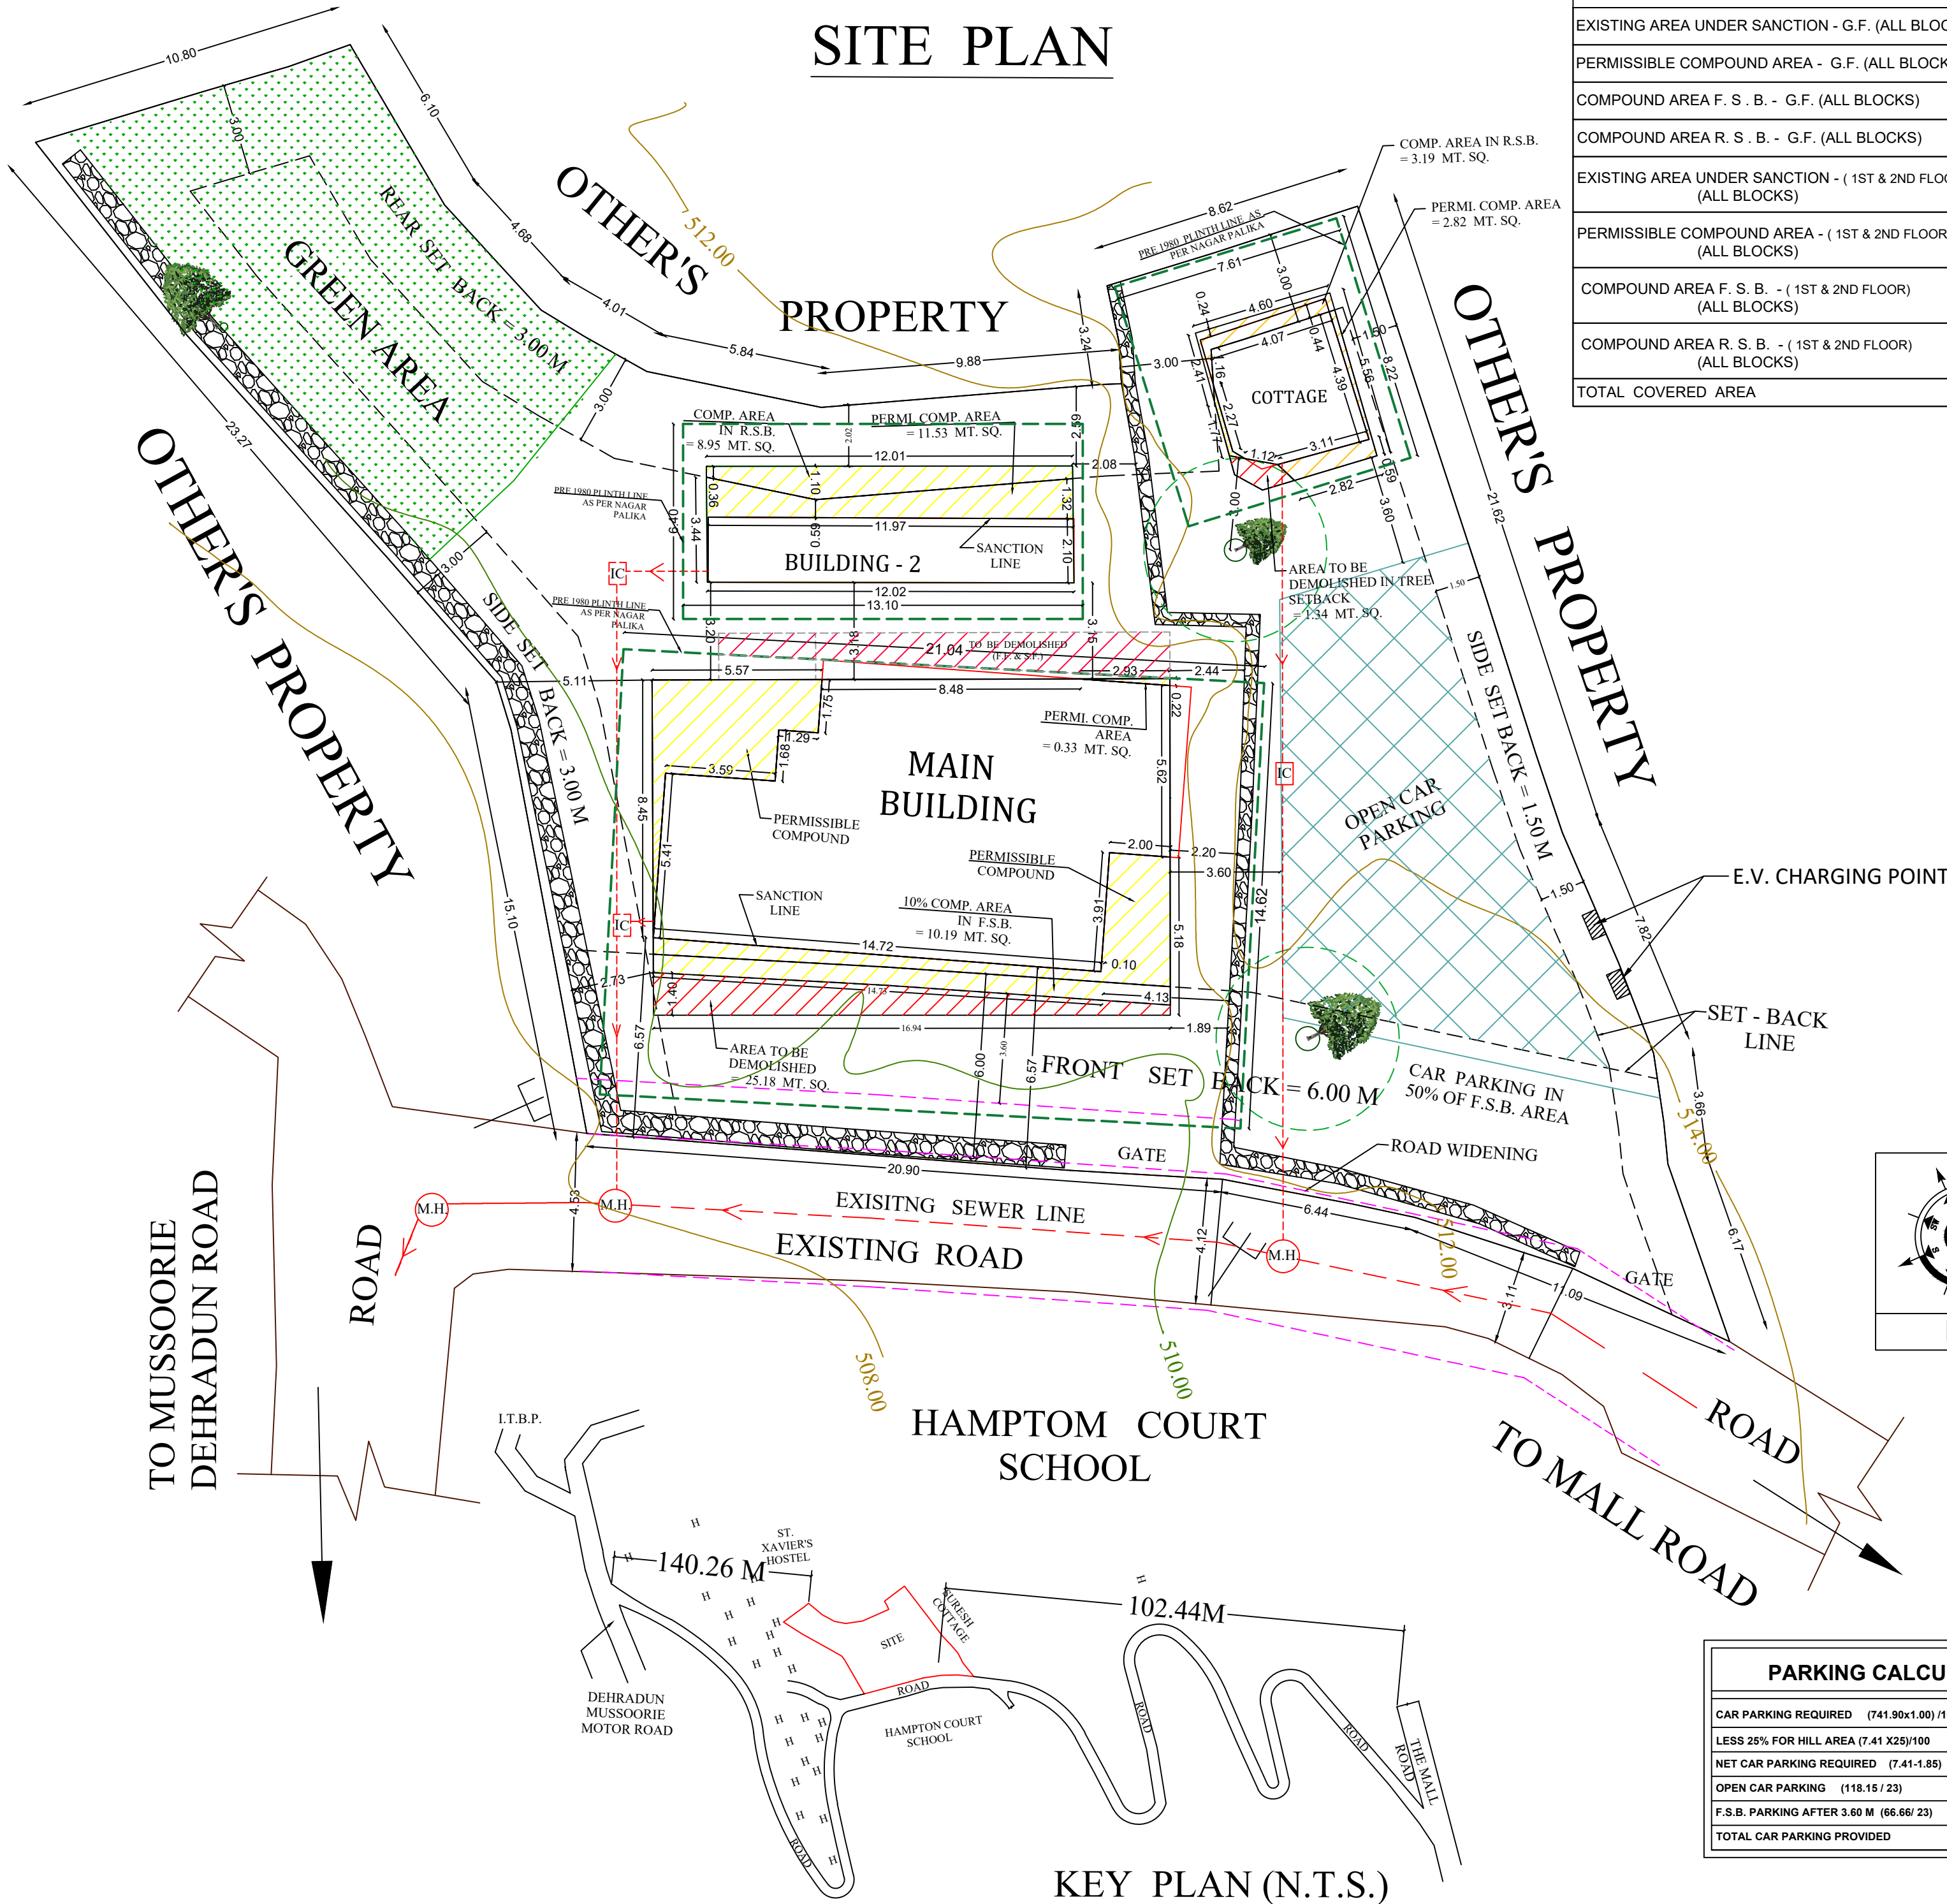

AREA STATEMENT FOR ALL BLOCKS TOGETHER	
EXISTING AREA UNDER SANCTION - G.F. (ALL BLOCKS)	= 172.76 SQ. MT.
PERMISSIBLE COMPOUND AREA - G.F. (ALL BLOCKS)	= 45.95 SQ. MT.
COMPOUND AREA F. S. B. - G.F. (ALL BLOCKS)	= 10.19 SQ. MT.
COMPOUND AREA R. S. B. - G.F. (ALL BLOCKS)	= 12.14 SQ. MT.
EXISTING AREA UNDER SANCTION - (1ST & 2ND FLOOR) (ALL BLOCKS)	= 345.52 SQ. MT.
PERMISSIBLE COMPOUND AREA - (1ST & 2ND FLOOR) (ALL BLOCKS)	= 110.68 SQ. MT.
COMPOUND AREA F. S. B. - (1ST & 2ND FLOOR) (ALL BLOCKS)	= 20.38 SQ. MT.
COMPOUND AREA R. S. B. - (1ST & 2ND FLOOR) (ALL BLOCKS)	= 24.28 SQ. MT.
TOTAL COVERED AREA	= 741.90 SQ. MT.

FOR M.D.D.A. USE	
COMPOUNDING MAP OF RECONSTRUCTED GUEST HOUSE BUILDING OF (1). MRS. RAJNI KUKREJA W/O LATE MR. MOHAN KUKREJA & (2). MR. SANJAY KUKREJA S/O LATE MR. MOHAN KUKREJA, DOON VIEW COTTAGE, HAMPTON COURT ROAD, MUSSOORIE, DIST: DEHRADUN, UTTARAKHAND	
AREA STATEMENT	
TOTAL PLOT AREA (AS PER SALEDEED)	1839.00 SQ.MT.
PLOT AREA OF GIFTED PORTION	840.00 SQ.MT.
TOTAL PLOT AREA OF REMAINING PORTION as per deed	999.00 SQ.MT.
ROAD WIDENING AREA	15.64 SQ.MT.
NET PLOT AREA	983.36 SQ.MT.
GROUND FLOOR AREA : MAIN BUILDING	
EXISTING COV. AREA UNDER SANCTION	129.30 SQ.MT.
AREA UNDER PERMISSIBLE COMP.	31.60 SQ.MT.
COMP. UNDER F.S.B.	10.19 SQ.MT.
TOTAL G.F. COVD. AREA (MAIN BUILDING)	171.09 SQ.MT.
GROUND FLOOR AREA : COTTAGE	
EXISTING COV. AREA UNDER SANCTION	18.12 SQ.MT.
AREA UNDER PERMISSIBLE COMP.	2.82 SQ.MT.
COMP. UNDER R.S.B.	3.19 SQ.MT.
TOTAL G.F. COVD. AREA (COTTAGE)	24.13 SQ.MT.
GROUND FLOOR AREA : BUILDING - 2	
EXISTING COV. AREA UNDER SANCTION	25.34 SQ.MT.
AREA UNDER PERMISSIBLE COMP.	11.53 SQ.MT.
COMP. UNDER R.S.B.	8.95 SQ.MT.
TOTAL G.F. COVD. AREA (BUILDING - 2)	45.82 SQ.MT.
TOTAL COVERED AREA GROUND FLOOR (MAIN BUILDING + BUILDING 2 + COTTAGE)	241.04 SQ.MT.
FIRST FLOOR AREA : MAIN BUILDING	
EXISTING COV. AREA UNDER SANCTION	129.30 SQ.MT.
AREA UNDER PERMISSIBLE COMP.	40.99 SQ.MT.
COMP. UNDER F.S.B.	10.19 SQ.MT.
TOTAL F.F. COVD. AREA (MAIN BUILDING)	180.48 SQ.MT.
FIRST FLOOR AREA : COTTAGE	
EXISTING COV. AREA UNDER SANCTION	18.12 SQ.MT.
AREA UNDER PERMISSIBLE COMP.	2.82 SQ.MT.
COMP. UNDER R.S.B.	3.19 SQ.MT.
TOTAL F.F. COVD. AREA (COTTAGE)	24.13 SQ.MT.
FIRST FLOOR AREA : BUILDING - 2	
EXISTING COV. AREA UNDER SANCTION	25.34 SQ.MT.
AREA UNDER PERMISSIBLE COMP.	11.53 SQ.MT.
COMP. UNDER R.S.B.	8.95 SQ.MT.
TOTAL F.F. COVD. AREA (BUILDING - 2)	45.82 SQ.MT.
TOTAL COVERED AREA FIRST FLOOR (MAIN BUILDING + BUILDING 2 + COTTAGE)	250.43 SQ.MT.
SECOND FLOOR AREA : MAIN BUILDING	
EXISTING COV. AREA UNDER SANCTION	129.30 SQ.MT.
AREA UNDER PERMISSIBLE COMP.	40.99 SQ.MT.
COMP. UNDER F.S.B.	10.19 SQ.MT.
TOTAL S.F. COVD. AREA (MAIN BUILDING)	180.48 SQ.MT.
SECOND FLOOR AREA : COTTAGE	
EXISTING COV. AREA UNDER SANCTION	18.12 SQ.MT.
AREA UNDER PERMISSIBLE COMP.	2.82 SQ.MT.
COMP. UNDER R.S.B.	3.19 SQ.MT.
TOTAL S.F. COVD. AREA (COTTAGE)	24.13 SQ.MT.
SECOND FLOOR AREA : BUILDING - 2	
EXISTING COV. AREA UNDER SANCTION	25.34 SQ.MT.
AREA UNDER PERMISSIBLE COMP.	11.53 SQ.MT.
COMP. UNDER R.S.B.	8.95 SQ.MT.
TOTAL S.F. COVD. AREA (BUILDING - 2)	45.82 SQ.MT.
TOTAL COVERED AREA SECOND FLOOR (MAIN BUILDING + BUILDING 2 + COTTAGE)	250.43 SQ.MT.
TOTAL COVERED AREA	741.90 SQ.MT.
OPEN LAND AREA	742.32 SQ.MT.
GROUND COVERAGE = (218.71 X 100) / 983.36 =	22.24 %
(PERMISSIBLE = 45%)	
F.A.R. = (675.43 / 983.36) (PERMISSIBLE = 1.35)	0.68
TOTAL AREA TO BE DEMOLISHED	80.69 SQ.MT.

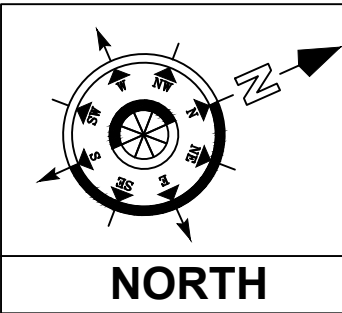

PARKING CALCULATION	
CAR PARKING REQUIRED (741.90x1.00)/100	7.41 E.C.S.
LESS 25% FOR HILL AREA (7.41 X25)/100	1.85 E.C.S.
NET CAR PARKING REQUIRED (7.41-1.85)	5.56 E.C.S.
OPEN CAR PARKING (118.15 / 23)	5.13 E.C.S.
F.S.B. PARKING AFTER 3.60 M (66.66/ 23)	2.89 E.C.S.
TOTAL CAR PARKING PROVIDED	8.02 E.C.S.

KEY PLAN (N.T.S.)

HEM CHANDRA DHOUNDIYAL
MDDA Lic.No.E/117/2022
Mob.No.9411140290

SIG. ARCHITECT


Rajni Kukreja

Sanjay


SIGN. OF OWNER

E: ASHISH DABRAL
P/UD (Civil Engineering) BT
Floorplan, M.Tech (Structural
Engineering), B.Tech (Civil Engineering)
Registration No. - DDN-LUGS-4/ ASSE-14/2002
P/UD-Kashwan Prast Barmah (I.A.)


SIG. OF STRUCTURE
ENGINEER

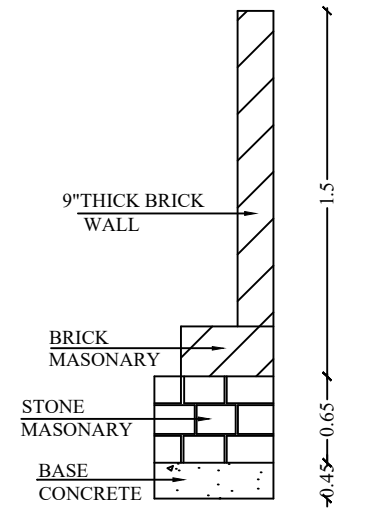


BAOUNADRY WALL
DETAILS

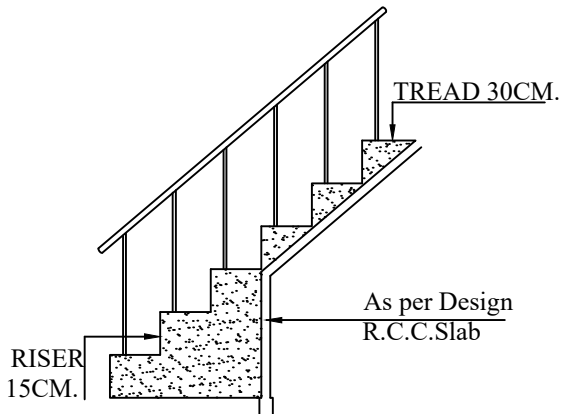


STAIRS DETAILS

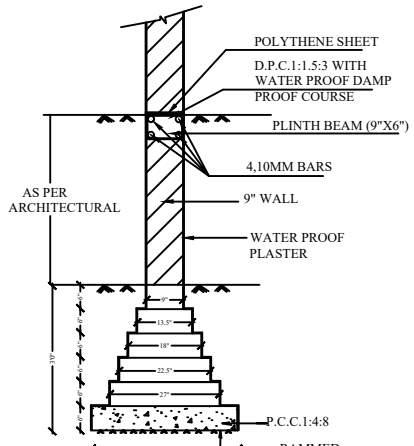

FOUNDATION DETAILS

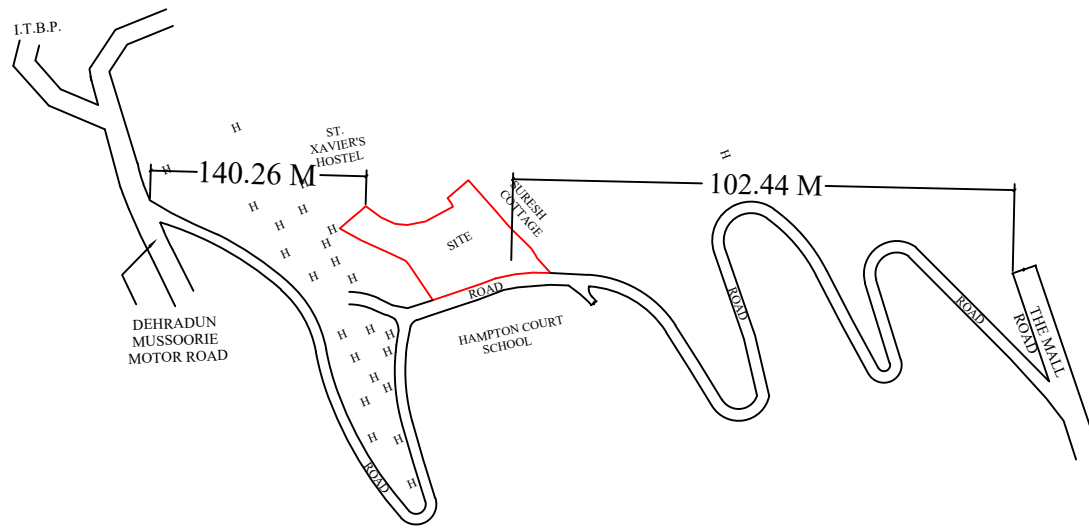

KEY PLAN
(N.T.S.)

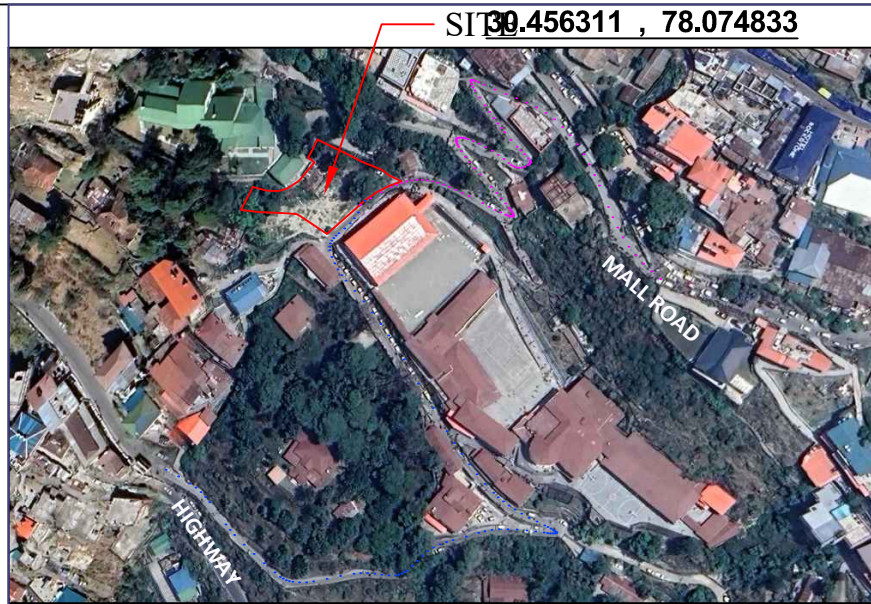

GOOGLE IMAGE OF SITE

FOR M.D.D.A. USE


COMPOUNDING MAP OF RECONSTRUCTED
GUEST HOUSE BUILDING OF (1). MRS.
RAJNI KUKREJA W/O LATE MR. MOHAN
KUKREJA & (2). MR. SANJAY KUKREJA S/O
LATE MR. MOHAN KUKREJA, DOON VIEW
COTTAGE, HAMPTON COURT ROAD,
MUSSOORIE, DIST: DEHRADUN,
UTTRAKHAND

SCHEDULE OF D/W

TYPE	WIDTH	HEIGHT	TYPE	WIDTH	HEIGHT
DOORS			WINDOWS		
D	1.00	2.10	W	1.80	1.56
D1	0.76	2.10	V	0.60	0.45
V	0.60	0.45			

LEGEND

R.W.H.T. - RAIN WATER HARVESTING TANK
I.C. - INSPECTION CHAMBER
N.T.S. - NOT TO SCALE

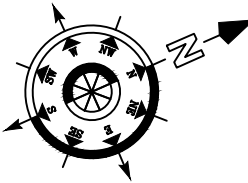

NORTH

Certified That :-

* The Building plans submitted for approval satisfy the safety requirements as stipulated in annexure-II and the given is factually correct to the best of our knowledge and understanding.

* The structural design including safety from natural hazard including earth-quake has been prepared by dully qualified structural engineer and these provisions shall be adhered to during the construction.

HEM CHANDRA DHOUDIYAL
MDDA Lic.No.E/117/2022
Mob.No.9411140290






SIG. ARCHITECT

Rajni Kukreja
Sanjay


SIG. OF OWNER

Dr. Ashish Dabral
PhD (Civil Engineering) IIT
Roorkee, M.Tech (Structural
Engineering), B.Tech (Civil Engineering)
Registration No. - DCH-UKG-1/ASE-18/2022
R/O-Kotdwara Post Garwal (U.K.)


SIG. OF STRUCTURE
ENGINEER

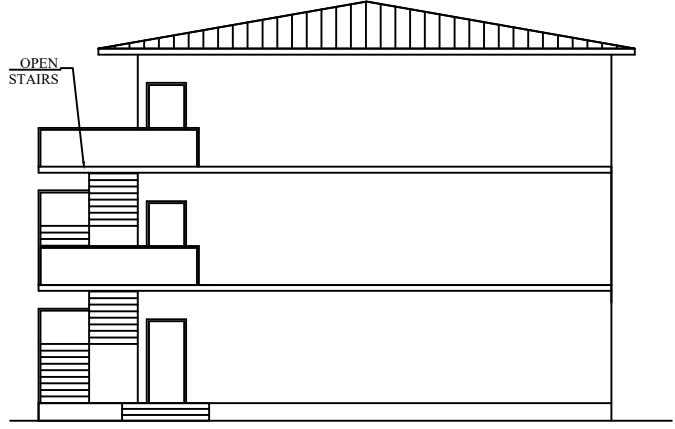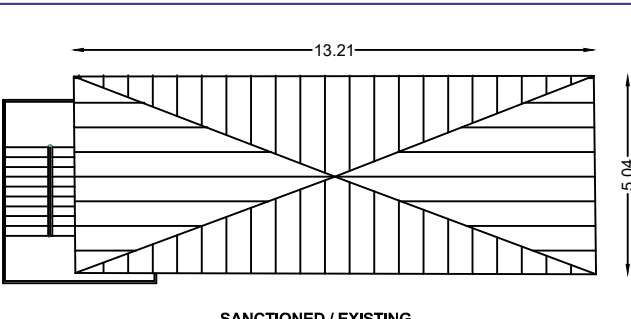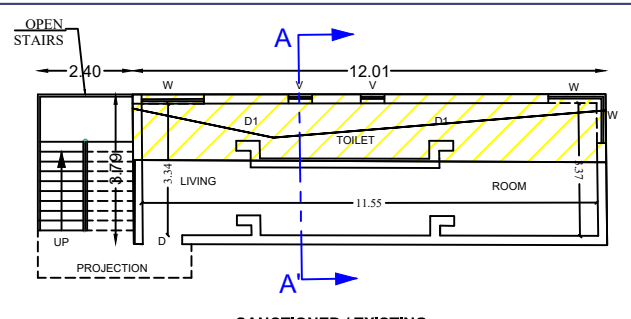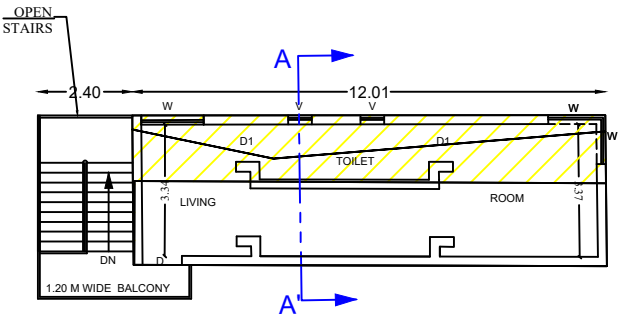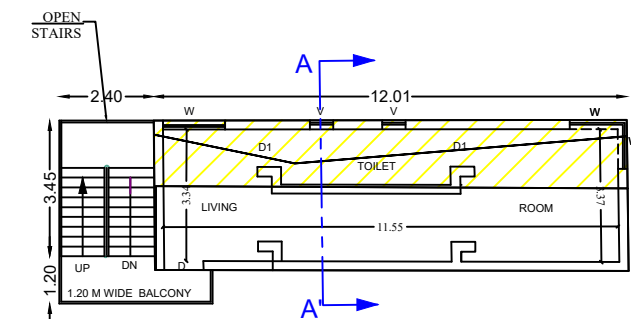


FRONT ELEVATION
(BUILDING - 2)

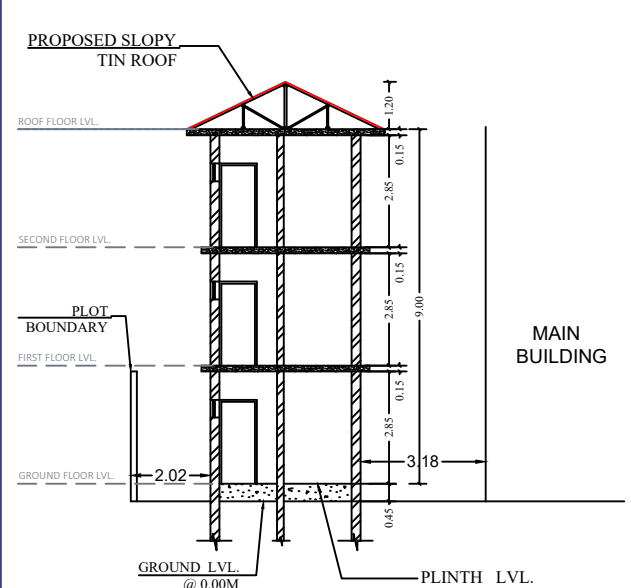


SECTION AT A-A'
(BUILDING - 2)

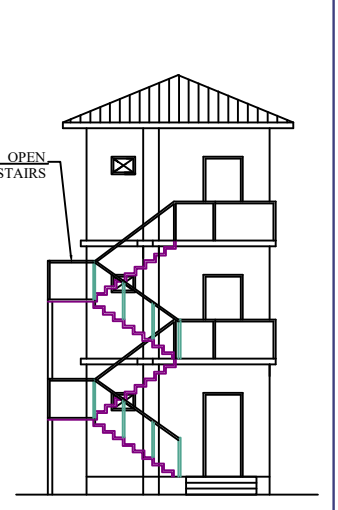


FRONT ELEVATION
(COTTAGE)

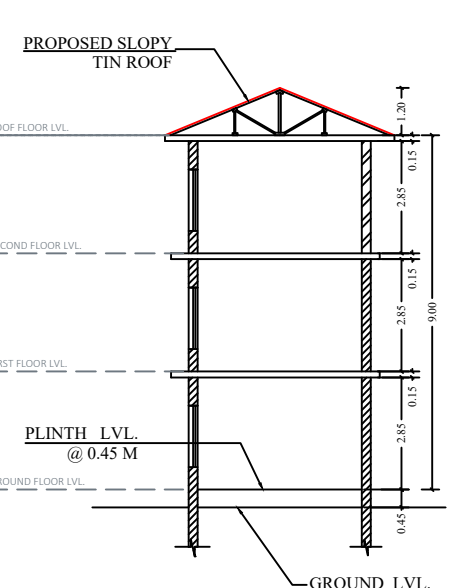


SECTION AT Y-Y'
(COTTAGE)

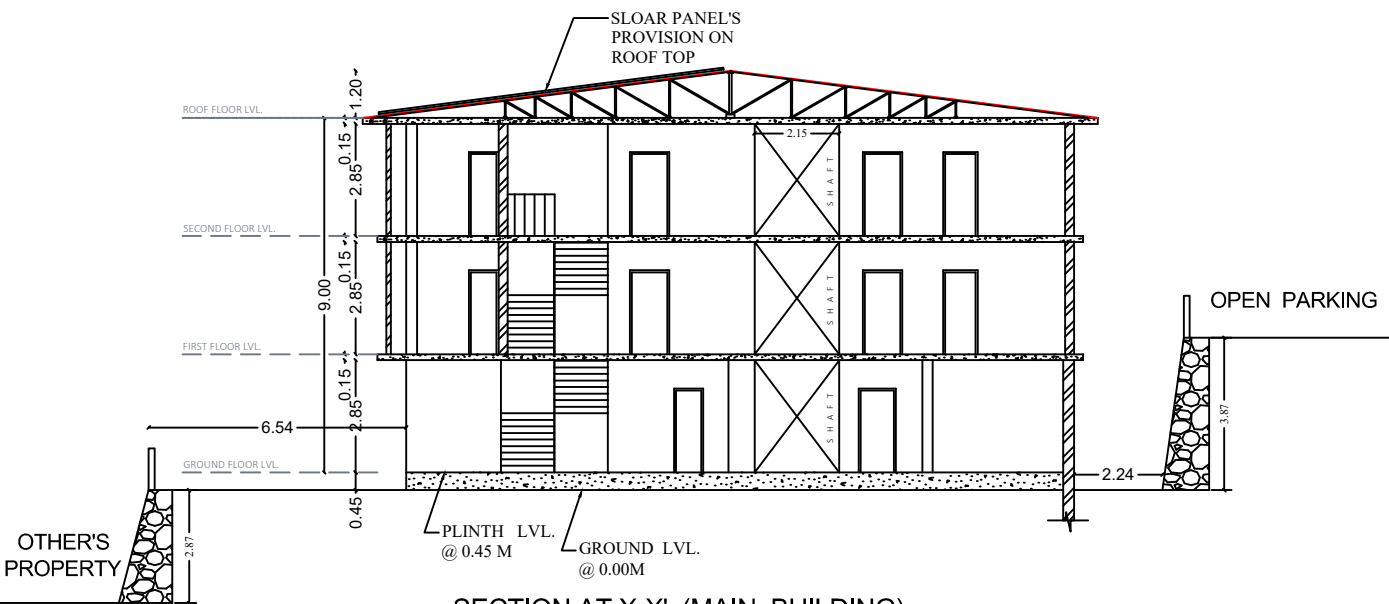


SECTION AT X-X' (MAIN BUILDING)

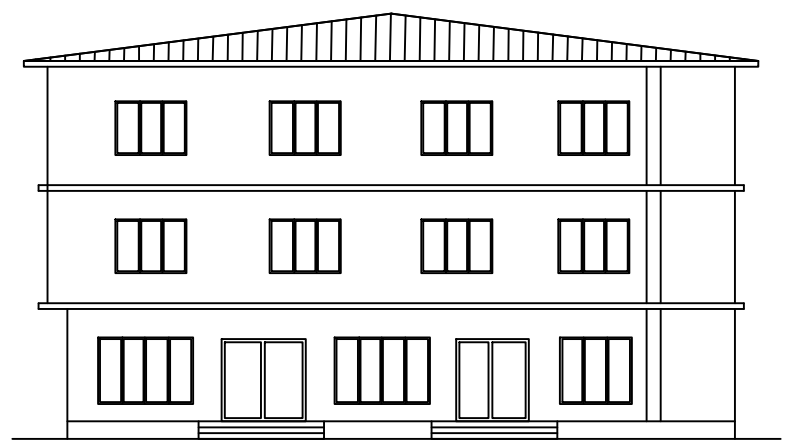


FRONT ELEVATION - MAIN BUILDING

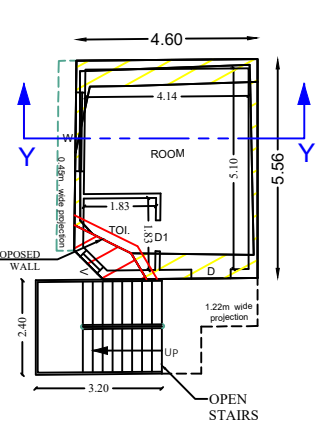


SANCTIONED / EXISTING
GROUND FLOOR PLAN
(COTTAGE)

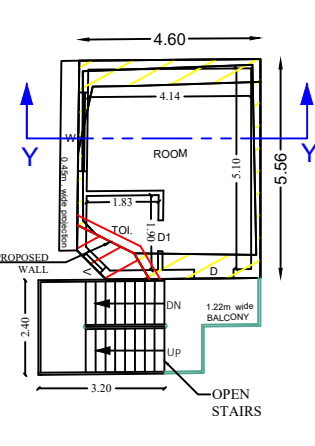


SANCTIONED / EXISTING
FIRST FLOOR PLAN
(COTTAGE)

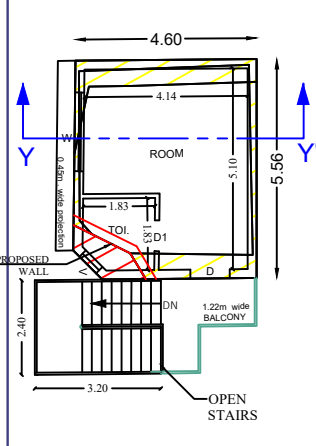


SANCTIONED / EXISTING
SECOND FLOOR PLAN
(COTTAGE)

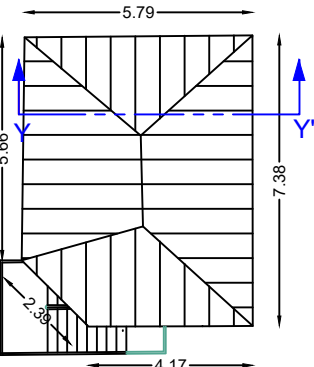


SLOPY ROOF PLAN
(COTTAGE)

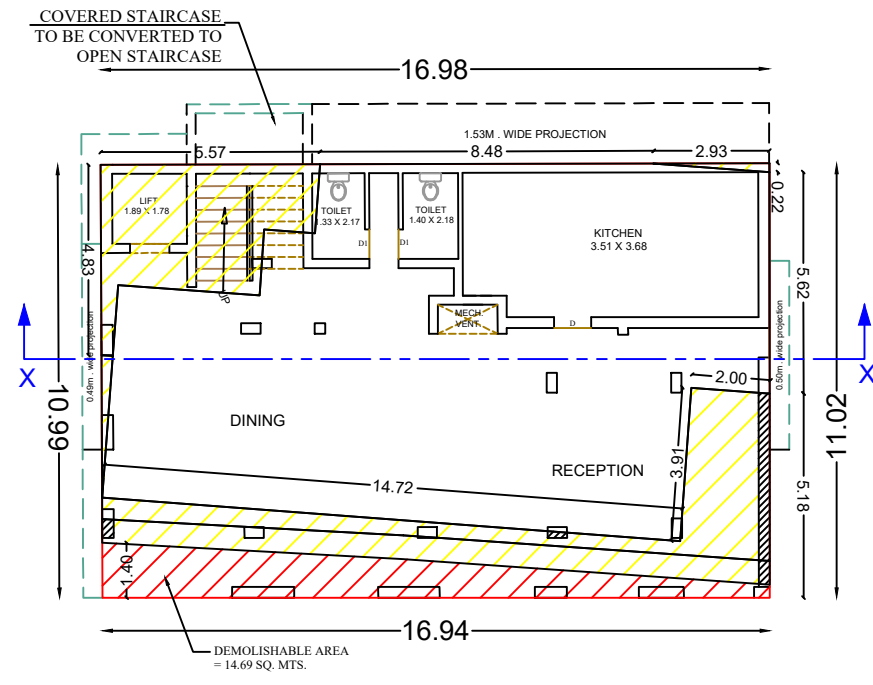


SANCTIONED / EXISTING
GROUND FLOOR PLAN (MAIN BUILDING)

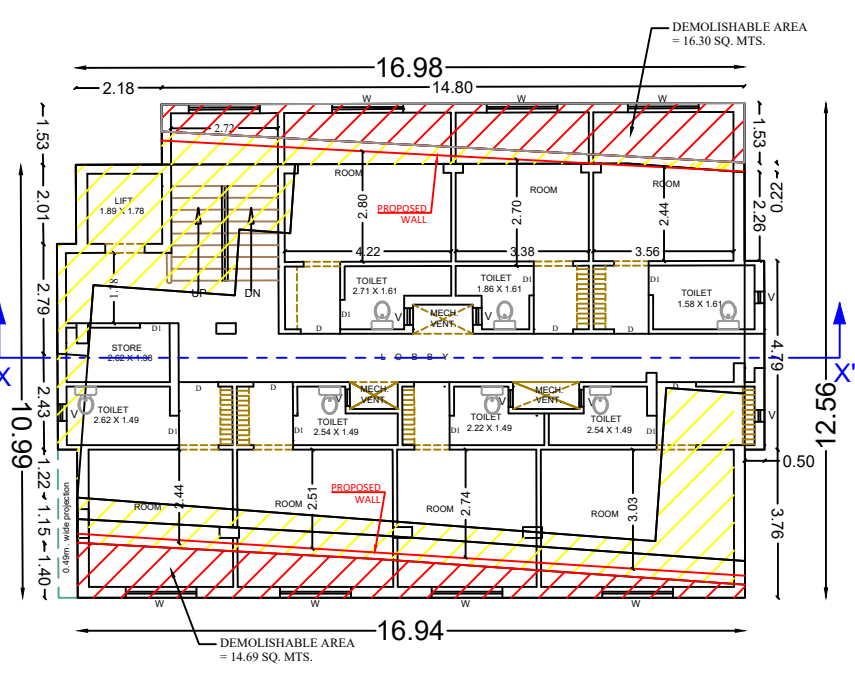

SANCTIONED / EXISTING
FIRST FLOOR PLAN (MAIN BUILDING)

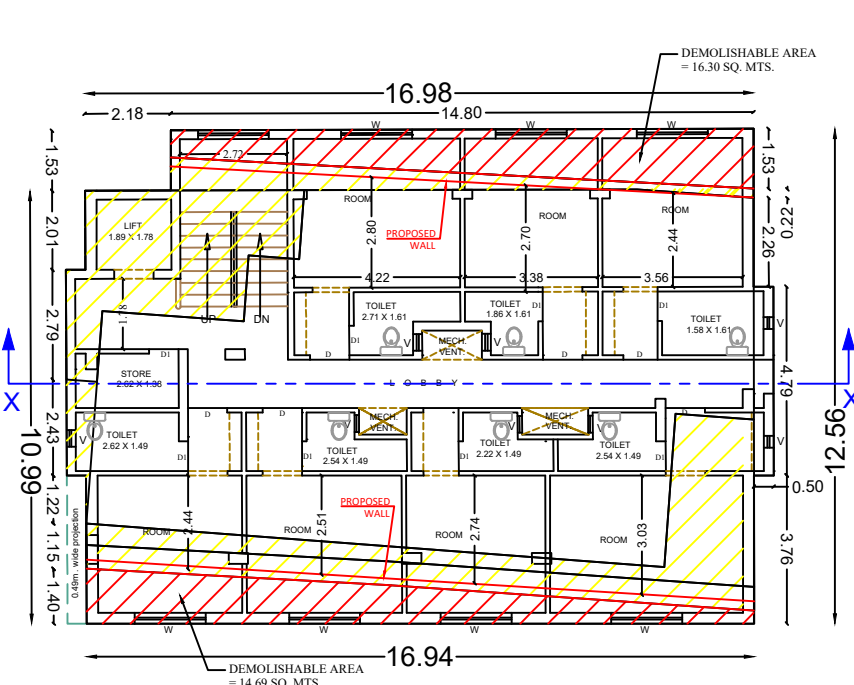

SANCTIONED / EXISTING
SECOND FLOOR PLAN (MAIN BUILDING)

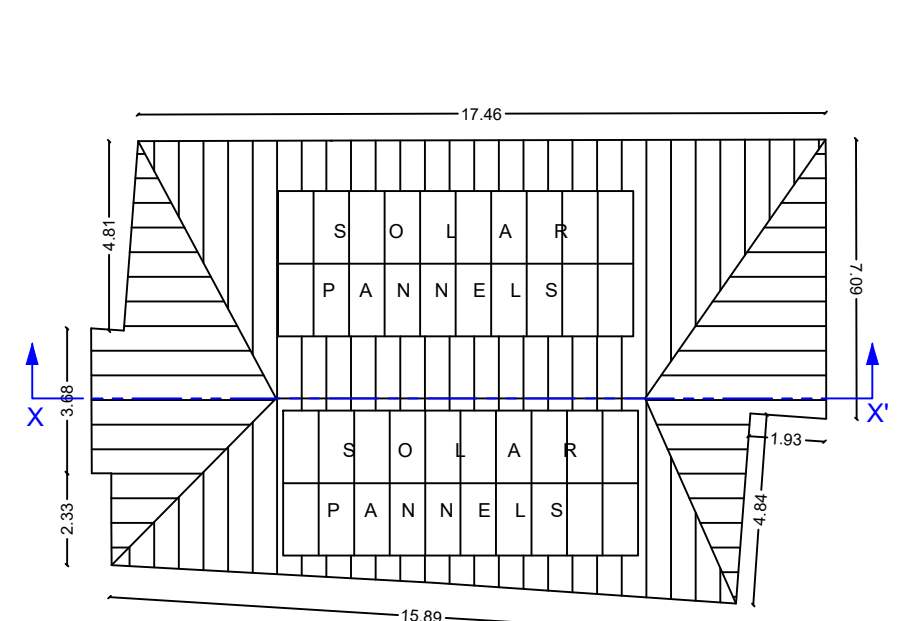

SLOPY ROOF PLAN (MAIN BUILDING)